


Skisse over rørføring dørmiljø Adgangskontrollert Tegningskode 1.9

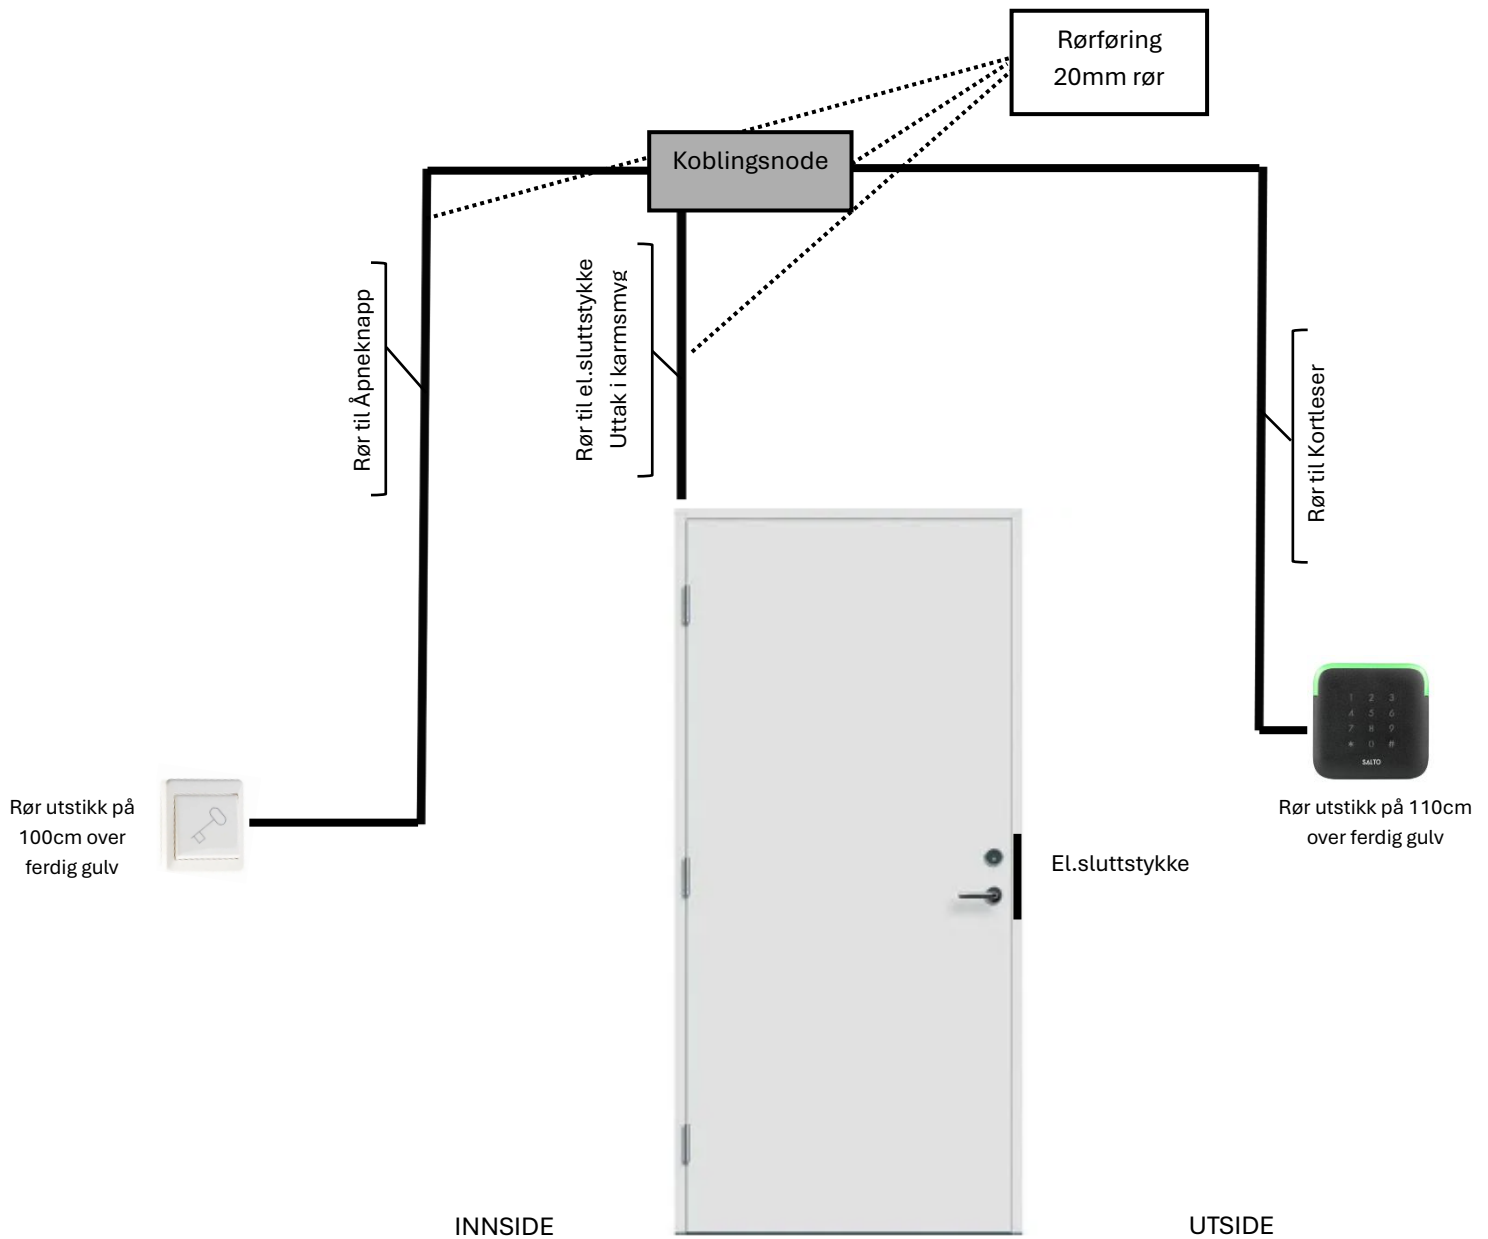

- Itlock trekker kabel i føringsveier levert av elektro.